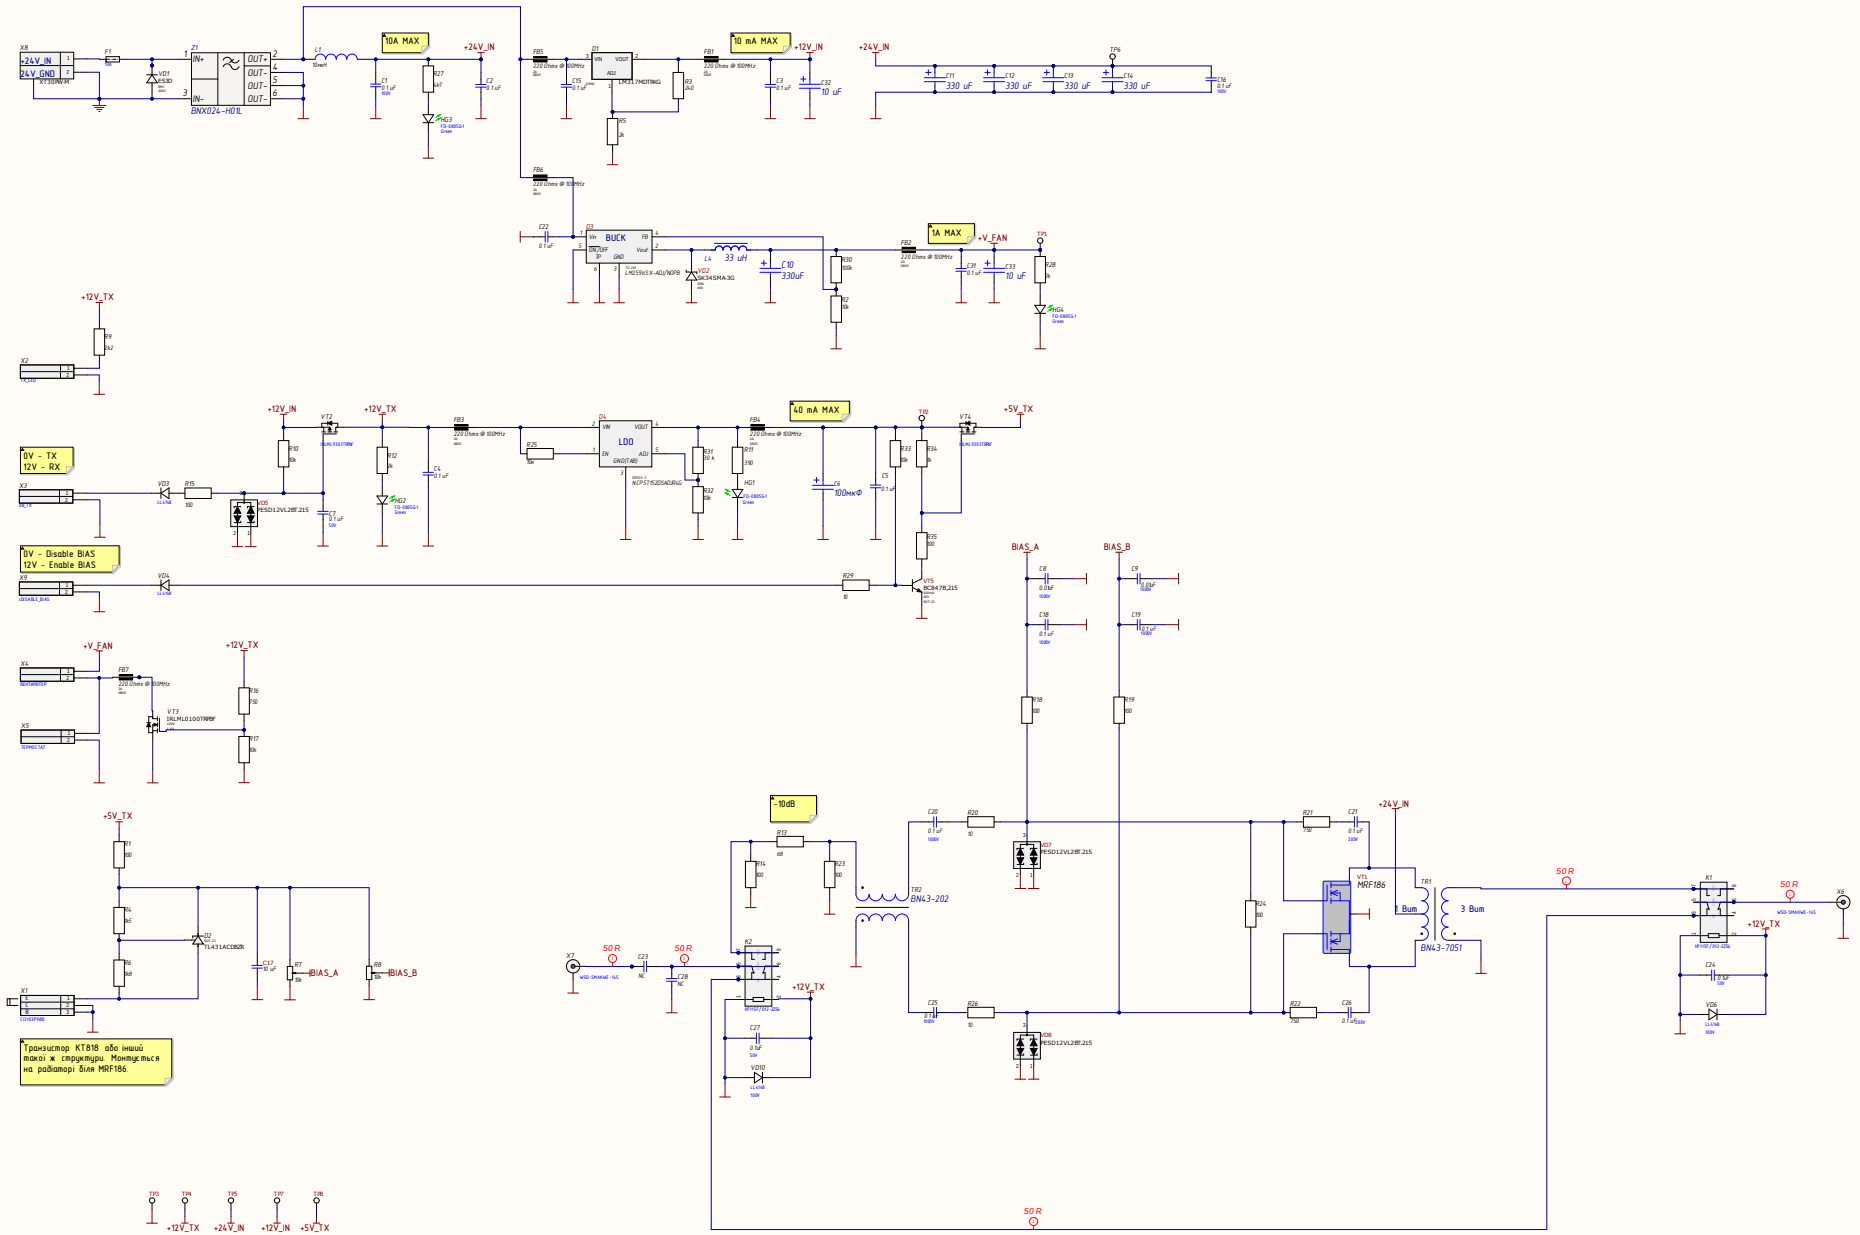


Изм.	Лист	№ докум.	Подп.	Дата	
Разраб.		Разработал			
Пров.		Проверил			
Т.контр.		Т. контр			
Нач.сект.		Нач. сектора			
Н.контр.		Н.Контр			
Утв.		Утвердил			

Децимальный номер ЭЗ

Наименование1
Наименование2
СХЕМА ЭЛЕКТРИЧЕСКАЯ
ПРИНЦИПИАЛЬНАЯ

Лит.	Масштаб	Масса
О		

Лист 1 Листов 1

Организация

Формат А1